Plan Form 2

**SIGNATURES AND SEALS ONLY**

THE COMMON SEAL OF BOOROWA RIVER PASTORAL CO PTY. LIMITED WAS HEREUNTO AFFIXED BY AUTHORITY OF THE DIRECTORS IN THE PRESENCE OF:

DIRECTOR

Seal

SECRETARY B E Queen

[illegible] IAN MUTUAL PROVIDENT SOCIETY by [illegible] Attorneys who have not received [illegible] revocation of the Power of Attorney [illegible] 166806 [illegible] Register under the authority of which [illegible] instrument has been [illegible] Sydney [illegible]

[illegible] sixth day of December 1976 [illegible] Development [illegible] Attorney [illegible] Power of Attorney [illegible] (Miscellaneous [illegible] and No. 120 [illegible] Titles Office who [illegible] that he has [illegible] notice of revocation of the power

Witness Assistant Manager [illegible]NEY

GORDON RAYMOND HAMMOND

JUSTICE OF THE PEACE

**Council Clerk's Certificate.**

*I hereby certify that—*

*(a) the requirements of the Local Government Act, 1919 (other than the requirements for the registration of plans), and*

**(b) ~~the requirements of section 34B of the †Metropolitan Water, Sewerage, and Drainage Act, 1924, as amended, †Hunter District Water, Sewerage, and Drainage Act, 1938, as amended,~~*

*have been complied with by the applicant in relation to the proposed* subdivision

*(Insert "new road", "subdivision" or "consolidated lot") set out herein.*

*Subdivision No.* 76/18

*Date* 17-11-76

*(Signature)*

*Council Clerk.*

**This part of certificate to be deleted where the application is only for a consolidated lot or the opening of a new road or where the land to be subdivided is wholly outside the areas of operations of the Metropolitan Water Sewerage and Drainage Board and the Hunter District Water Board.* *†Delete if inapplicable.*

**Plan Drawing only to appear in this space.**

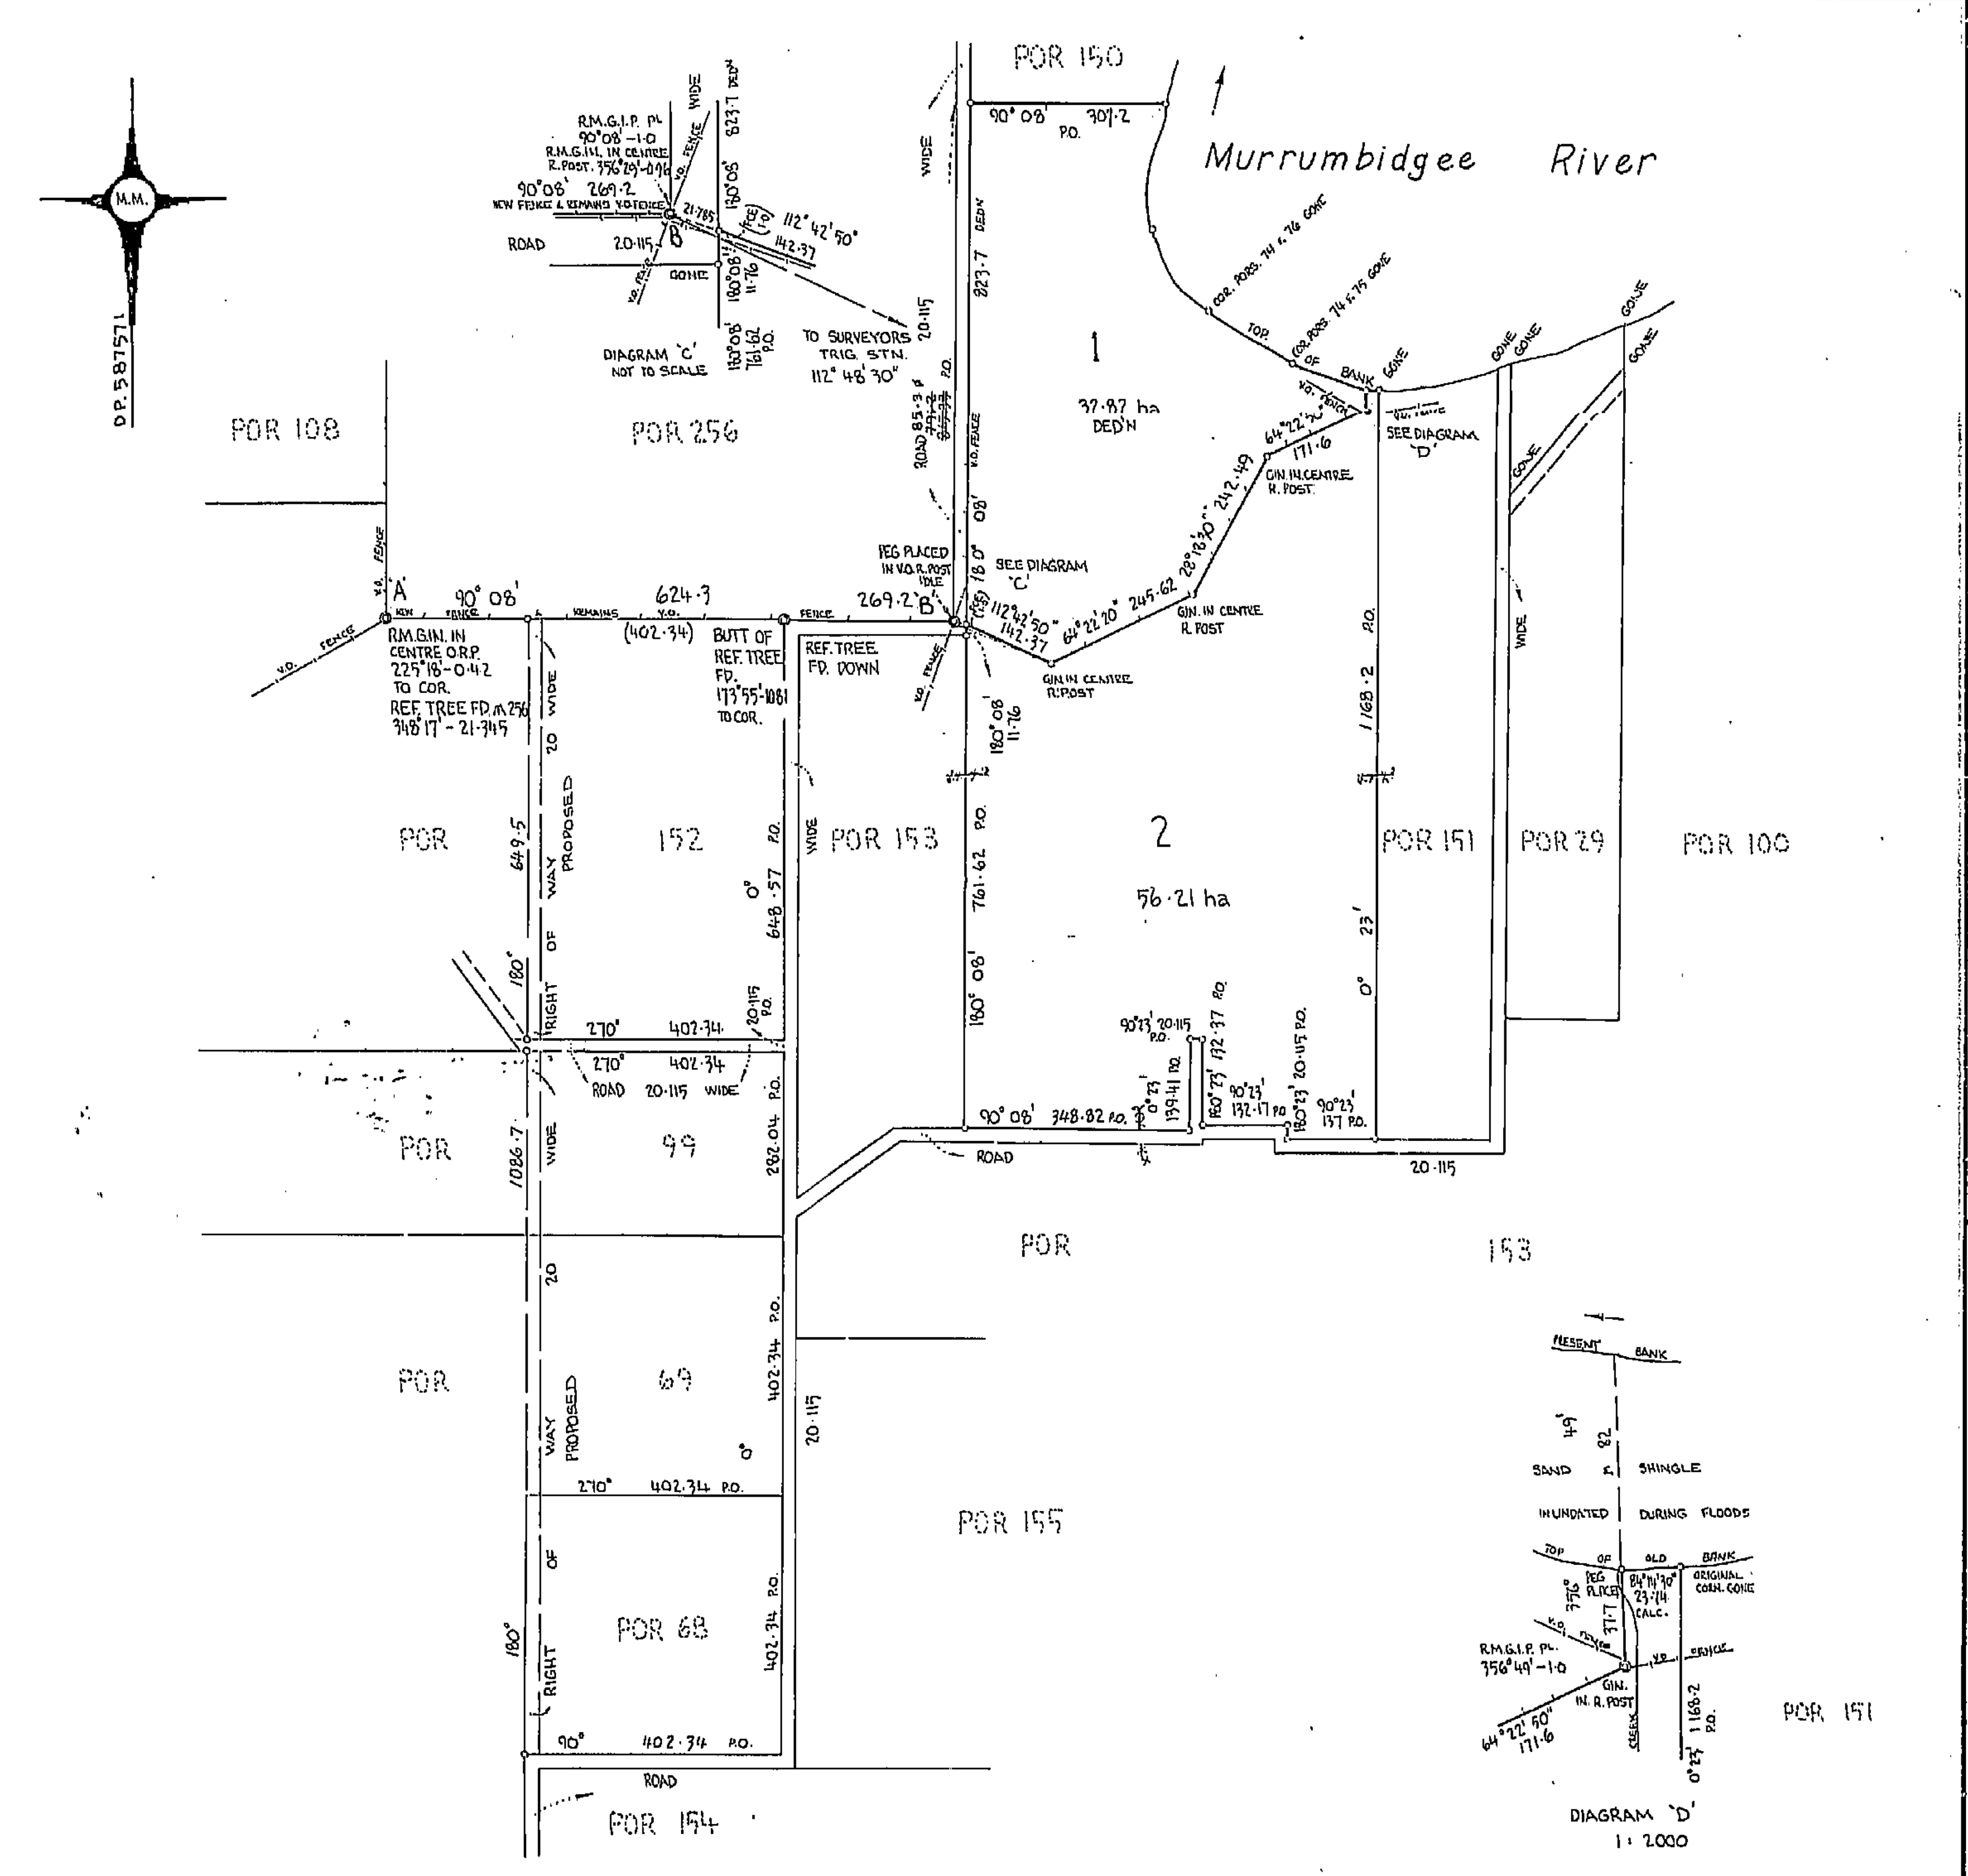

*OFFICE USE ONLY

D.P. 587571 *

Registered: 6-1-1977

C.A.: Nº 76/18 OF 17-11-1976

Title System: TORRENS

Purpose: SUBDIVISION

Ref. Map: PARISH *

Last Plan:

PLAN OF CONSOLIDATION & SUBDIVISION OF PORTIONS 74 75 76 AND PORTION 149

**Reduction Ratio 1:** 8 000

**Lengths are in metres.**

**~~Mun~~/Shire ~~City~~:** GOODRADIGBEE

**Locality:** THE HORSE SHOE

**Parish:** UMBURRA

**County:** COWLEY

**~~This is sheet 1 of my plan in~~ sheets.** ~~(Delete if inapplicable.)~~

I, ALLAN JEFFREY MAIL

of 35 MONKMAN STREET, CHAPMAN, A.C.T.

*a surveyor registered under the Surveyors Act, 1929, as amended, hereby certify that the survey represented in this plan is accurate and has been made *(1) by me ~~(2) under my immediate supervision~~ in accordance with the Survey Practice Regulations, 1933, and was completed on †* 10 NOVEMBER, 1976

*Signature*

*Surveyor registered under Surveyors Act, 1929, as amended.*
*Datum Line of Azimuth.* A — B
**Strike out either (1) or (2). †Insert date of survey.*

*Panel for use only for statements of intention to dedicate public roads or to create public reserves, drainage reserves, easements or restrictions as to user.*

N 0 0 2 A 1 A

PLAN AMENDED IN REG GEN OFFICE 6-4-1978

D.P. 587571

Table of mm

**WARNING: CREASING OR FOLDING WILL LEAD TO REJECTION**

*SURVEYOR'S REFERENCE:* 76/442

AMENDMENTS OR ADDITIONS NOTED ON PLAN IN REGISTRAR GENERAL'S OFFICE.

I, Bruce Richard Davies, Registrar General for New South Wales, certify that this negative is a photograph made as a permanent record of a document in my custody this 11th day of April, 1978