Plan Form 2

Plan Drawing only to appear in this space.

DP588350 *OFFICE USE ONLY

SIGNATURES AND SEALS ONLY

AUSTRALIAN MUTUAL PROVIDENT SO[illegible] [illegible] undersigned Attorneys who have not received [illegible] of the revocation of the Power of Attorney registered No. 161806 [illegible] under the authority of which this instrument has been executed [illegible] by the

ALLAN CHARLES BUTCHART

~~LEIGH LODDINGTON~~ HALL

LODGEDALE PTY. LIMITED Common Seal

Director.

The Common Seal of Lodgedale PTY. LIMITED was hereto affixed by authority of the Directors in the presence of

R E Owen Secretary.

THE COMMON SEAL OF THE HORSESHOE PTY LIMITED WAS HEREUNTO AFFIXED IN ACCORDANCE WITH ITS ARTICLES OF ASSOCIATION AND IN THE PRESENCE OF

THE HORSESHOE PTY. LIMITED Common Seal

DIRECTOR

A. Gillespie-Jones
SECRETARY.

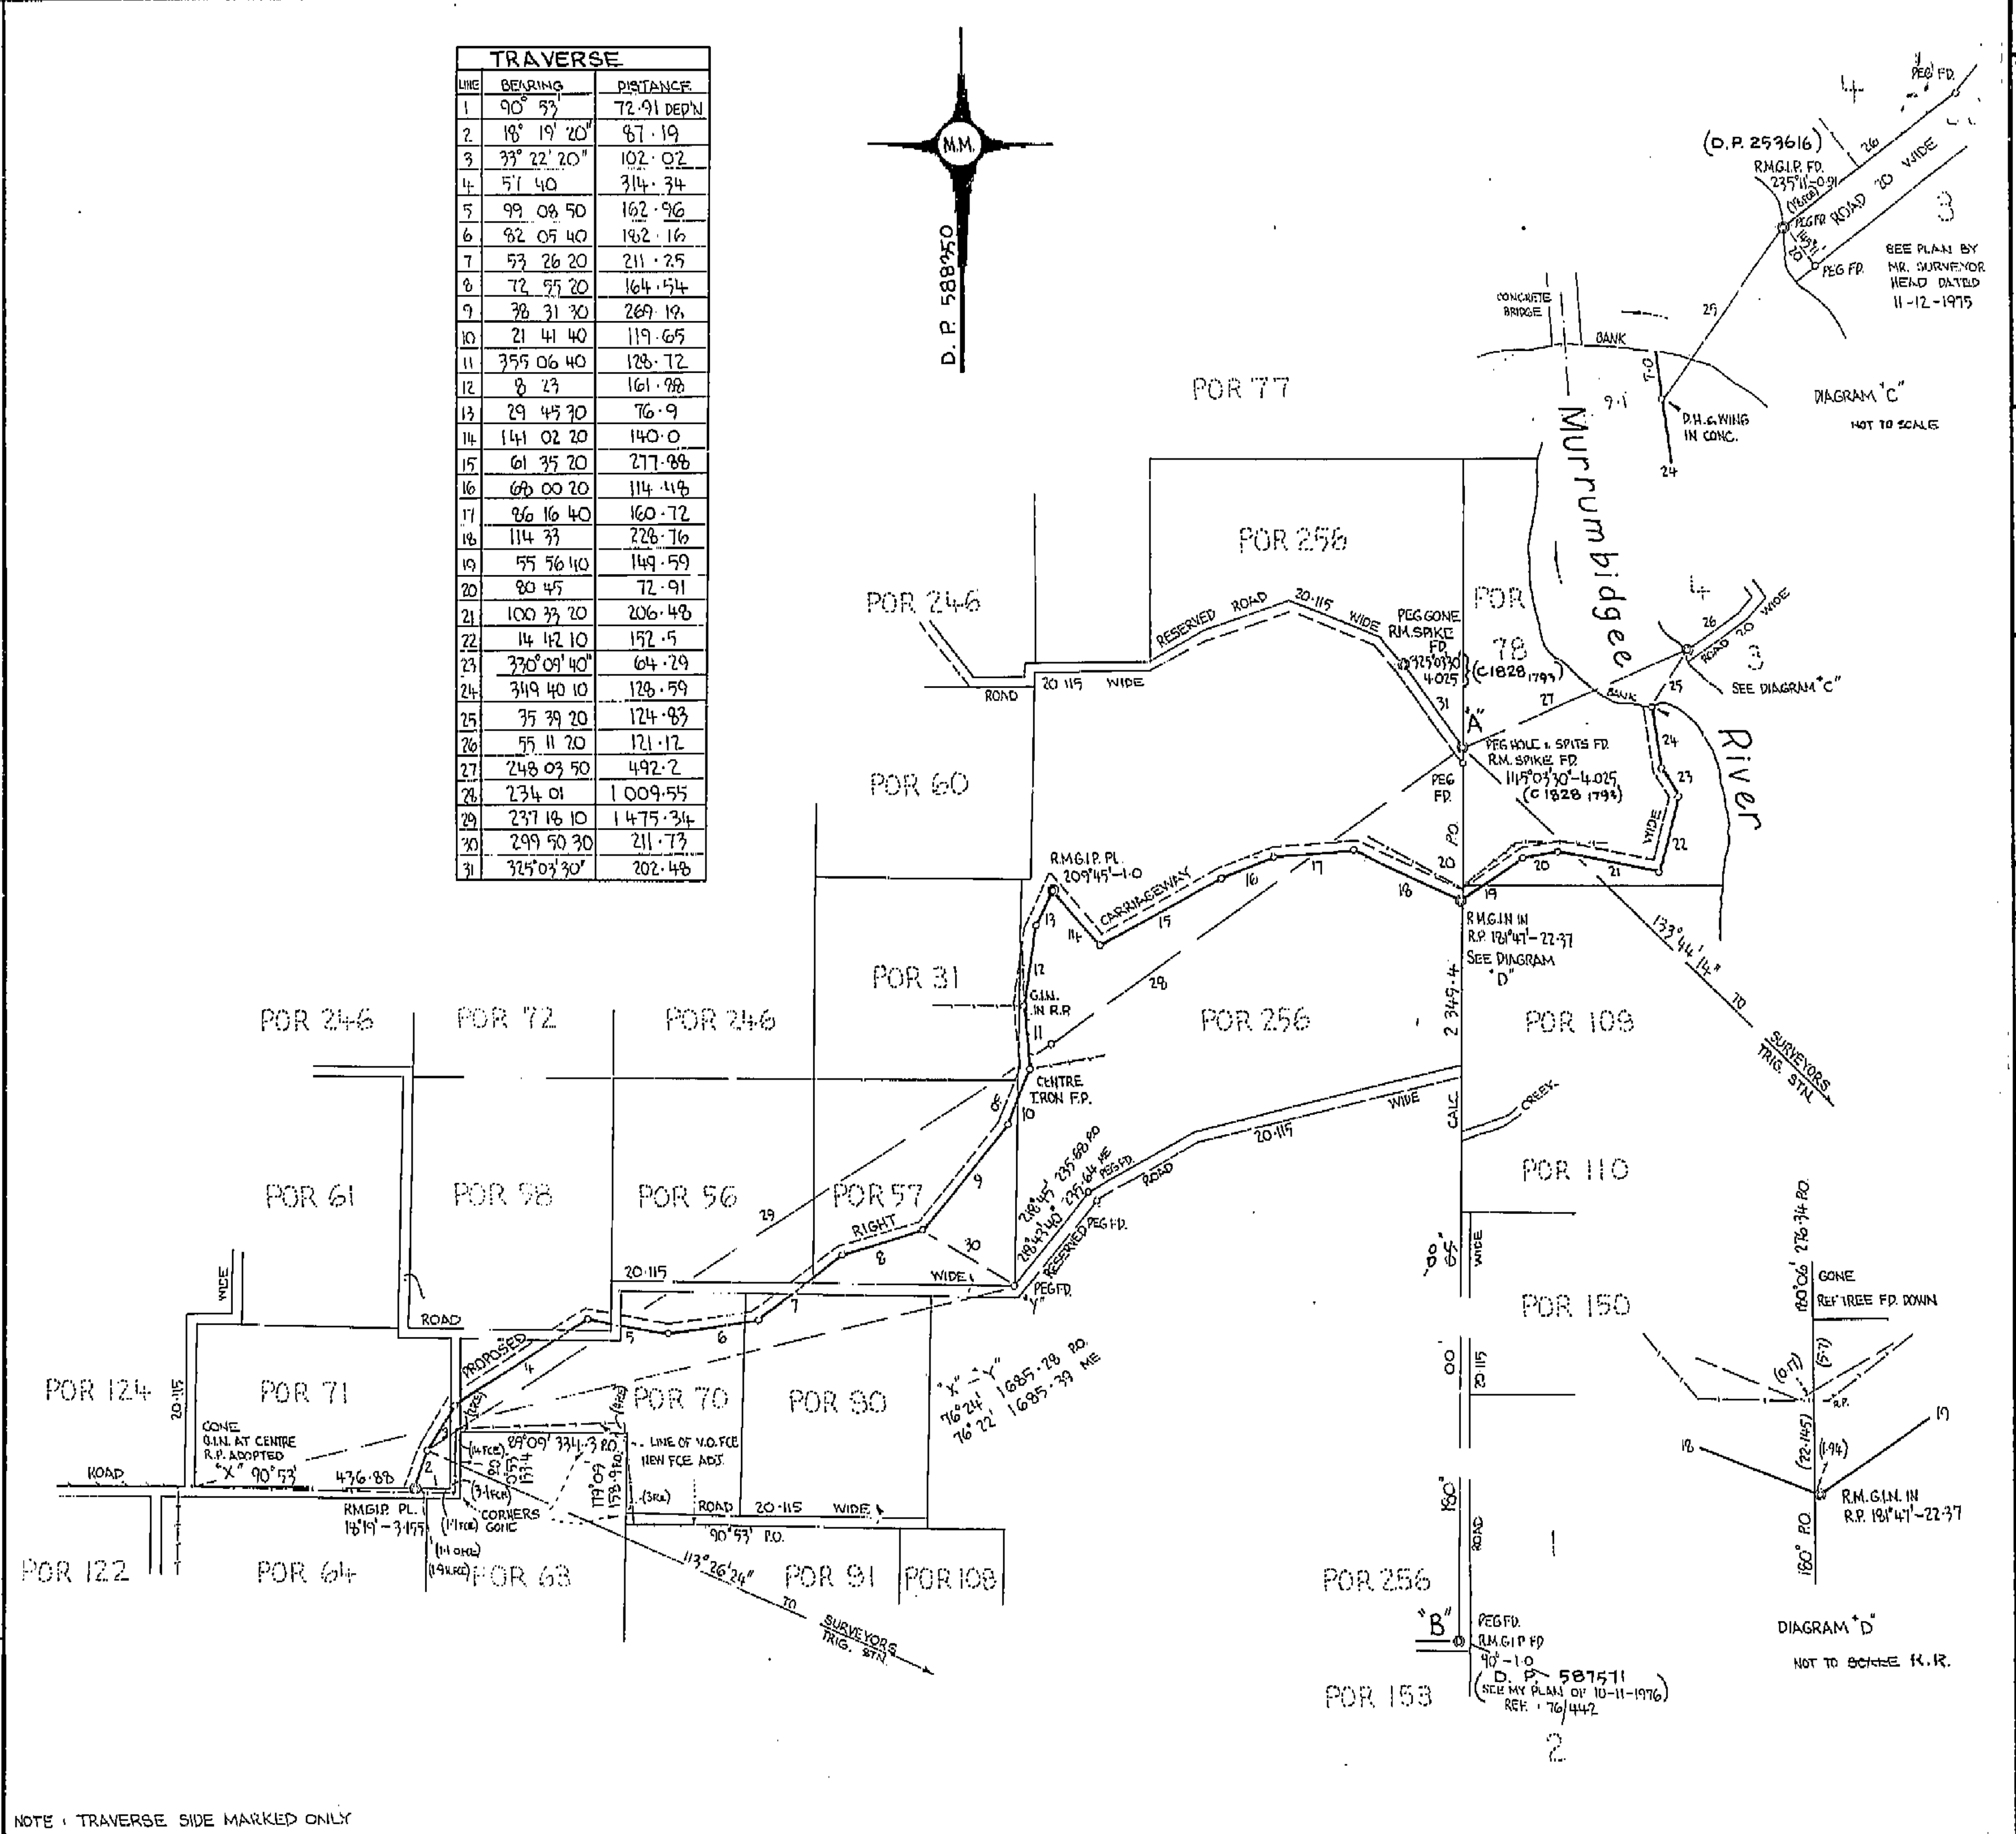

TRAVERSE		
LINE	BEARING	DISTANCE
1	90° 53'	72·91 DEP'N
2	18° 19' 20"	87·19
3	33° 22' 20"	102·02
4	51 40	314·34
5	99 08 50	162·96
6	82 05 40	182·16
7	53 26 20	211·25
8	72 55 20	164·54
9	38 31 30	269·19
10	21 41 40	119·65
11	355 06 40	128·72
12	8 23	161·98
13	29 45 30	76·9
14	141 02 20	140·0
15	61 35 20	277·88
16	68 00 20	114·48
17	86 16 40	160·72
18	114 33	228·76
19	55 56 40	149·59
20	80 45	72·91
21	100 33 20	206·48
22	14 42 10	152·5
23	330° 09' 40"	64·29
24	349 40 10	128·59
25	35 39 20	124·83
26	55 11 20	121·12
27	248 03 50	492·2
28	234 01	1 009·55
29	237 18 10	1 475·34
30	299 50 30	211·73
31	325° 03' 30"	202·48

NOTE : TRAVERSE SIDE MARKED ONLY

D.P. 588350 *

N O O O F I A

Registered: [illegible] 22.3.1977

~~C.A.:~~

Title System: TORRENS

Purpose: EASEMENT

Ref. Map: PARISH

Last Plan: ——

PLAN OF PROPOSED RIGHT OF CARRIAGEWAY 20 WIDE OVER PORTIONS 31, 56, 57, 58, 70, 71, 78, 90, 109 AND 256.

Reduction Ratio 1: 10 000
Lengths are in metres.

~~Mun.~~/Shire ~~City~~ GOODRADIGBEE

Locality: HAWTHORN

Parish: UMBURRA

County: COWLEY

~~**This is sheet 1 of my plan in**~~ **sheets.**
(Delete if inapplicable.)

I, ALLAN JEFFREY MAIL

of 35 MONKMAN STREET, CHAPMAN, A.C.T.

*a surveyor registered under the Surveyors Act, 1929, as amended, hereby certify that the survey represented in this plan is accurate and has been made *(1) by me ~~(2) under my immediate supervision~~ in accordance with the Survey Practice Regulations, 1933, and was completed on †* 20 DECEMBER, 1976.

Signature A J Mail

Surveyor registered under Surveyors Act, 1929, as amended.
Datum Line of Azimuth. "A"—"B"
**Strike out either (1) or (2). †Insert date of survey.*

Panel for use only for statements of intention to dedicate public roads or to create public reserves, drainage reserves, easements or restrictions as to user.

Council Clerk's Certificate.

I hereby certify that—

(a) the requirements of the Local Government Act, 1919 (other than the requirements for the registration of plans), and

**(b) the requirements of section 34B of the †Metropolitan Water, Sewerage, and Drainage Act, 1924, as amended, †Hunter District Water, Sewerage, and Drainage Act, 1938, as amended,*

have been complied with by the applicant in relation to the proposed ……………
(insert "new road", "subdivision" or "consolidated lot") set out herein.

Subdivision No.……………

Date……………

(Signature)……………
Council Clerk.

**This part of certificate to be deleted where the application is only for a consolidated lot or the opening of a new road or where the land to be subdivided is wholly outside the areas of operations of the Metropolitan Water Sewerage and Drainage Board and the Hunter District Water Board. †Delete if inapplicable.*

10	20	30	40	50	60	70	80	90	100	110	120	130	140	150	160	170	*Table of mm*	220	230	240	250	260	270	280	290	300	310	320	330	340	350	360	370	380	390		

WARNING: CREASING OR FOLDING WILL LEAD TO REJECTION

SURVEYOR'S REFERENCE: 76/449

M.P.D.

I, Bruce Richard Davies, Registrar General for New South Wales, certify that this negative is a photograph made as a permanent record of a document in my custody this 24th day of March, 1977