Req:R339551 /Doc:DP 0639390 P /Rev:15-Dec-1992 /NSW LRS /Pgs:ALL /Prt:28-Nov-2025 16:30 /Seq:1 of 1
© Office of the Registrar-General /Src:Fynd /Ref:Murrumbella

PLAN FORM 2

Plan Drawing only to appear in this space

*OFFICE USE ONLY

Signatures and seals only.


The common seal of The Horseshoe Pty Limited was hereunto affixed by authority of the Board of Directors in the presence of

November 1986

WILLIAM JAMES BURTON
JUSTICE OF THE PEACE

20th November 1986 For Commonwealth ... appointed Attorney ... Power of Attorney ... No. ... who ... has not received notice of revocation

Witness
J.G. BLACK, J.P.
JOHN WILLIAM DIMENTO

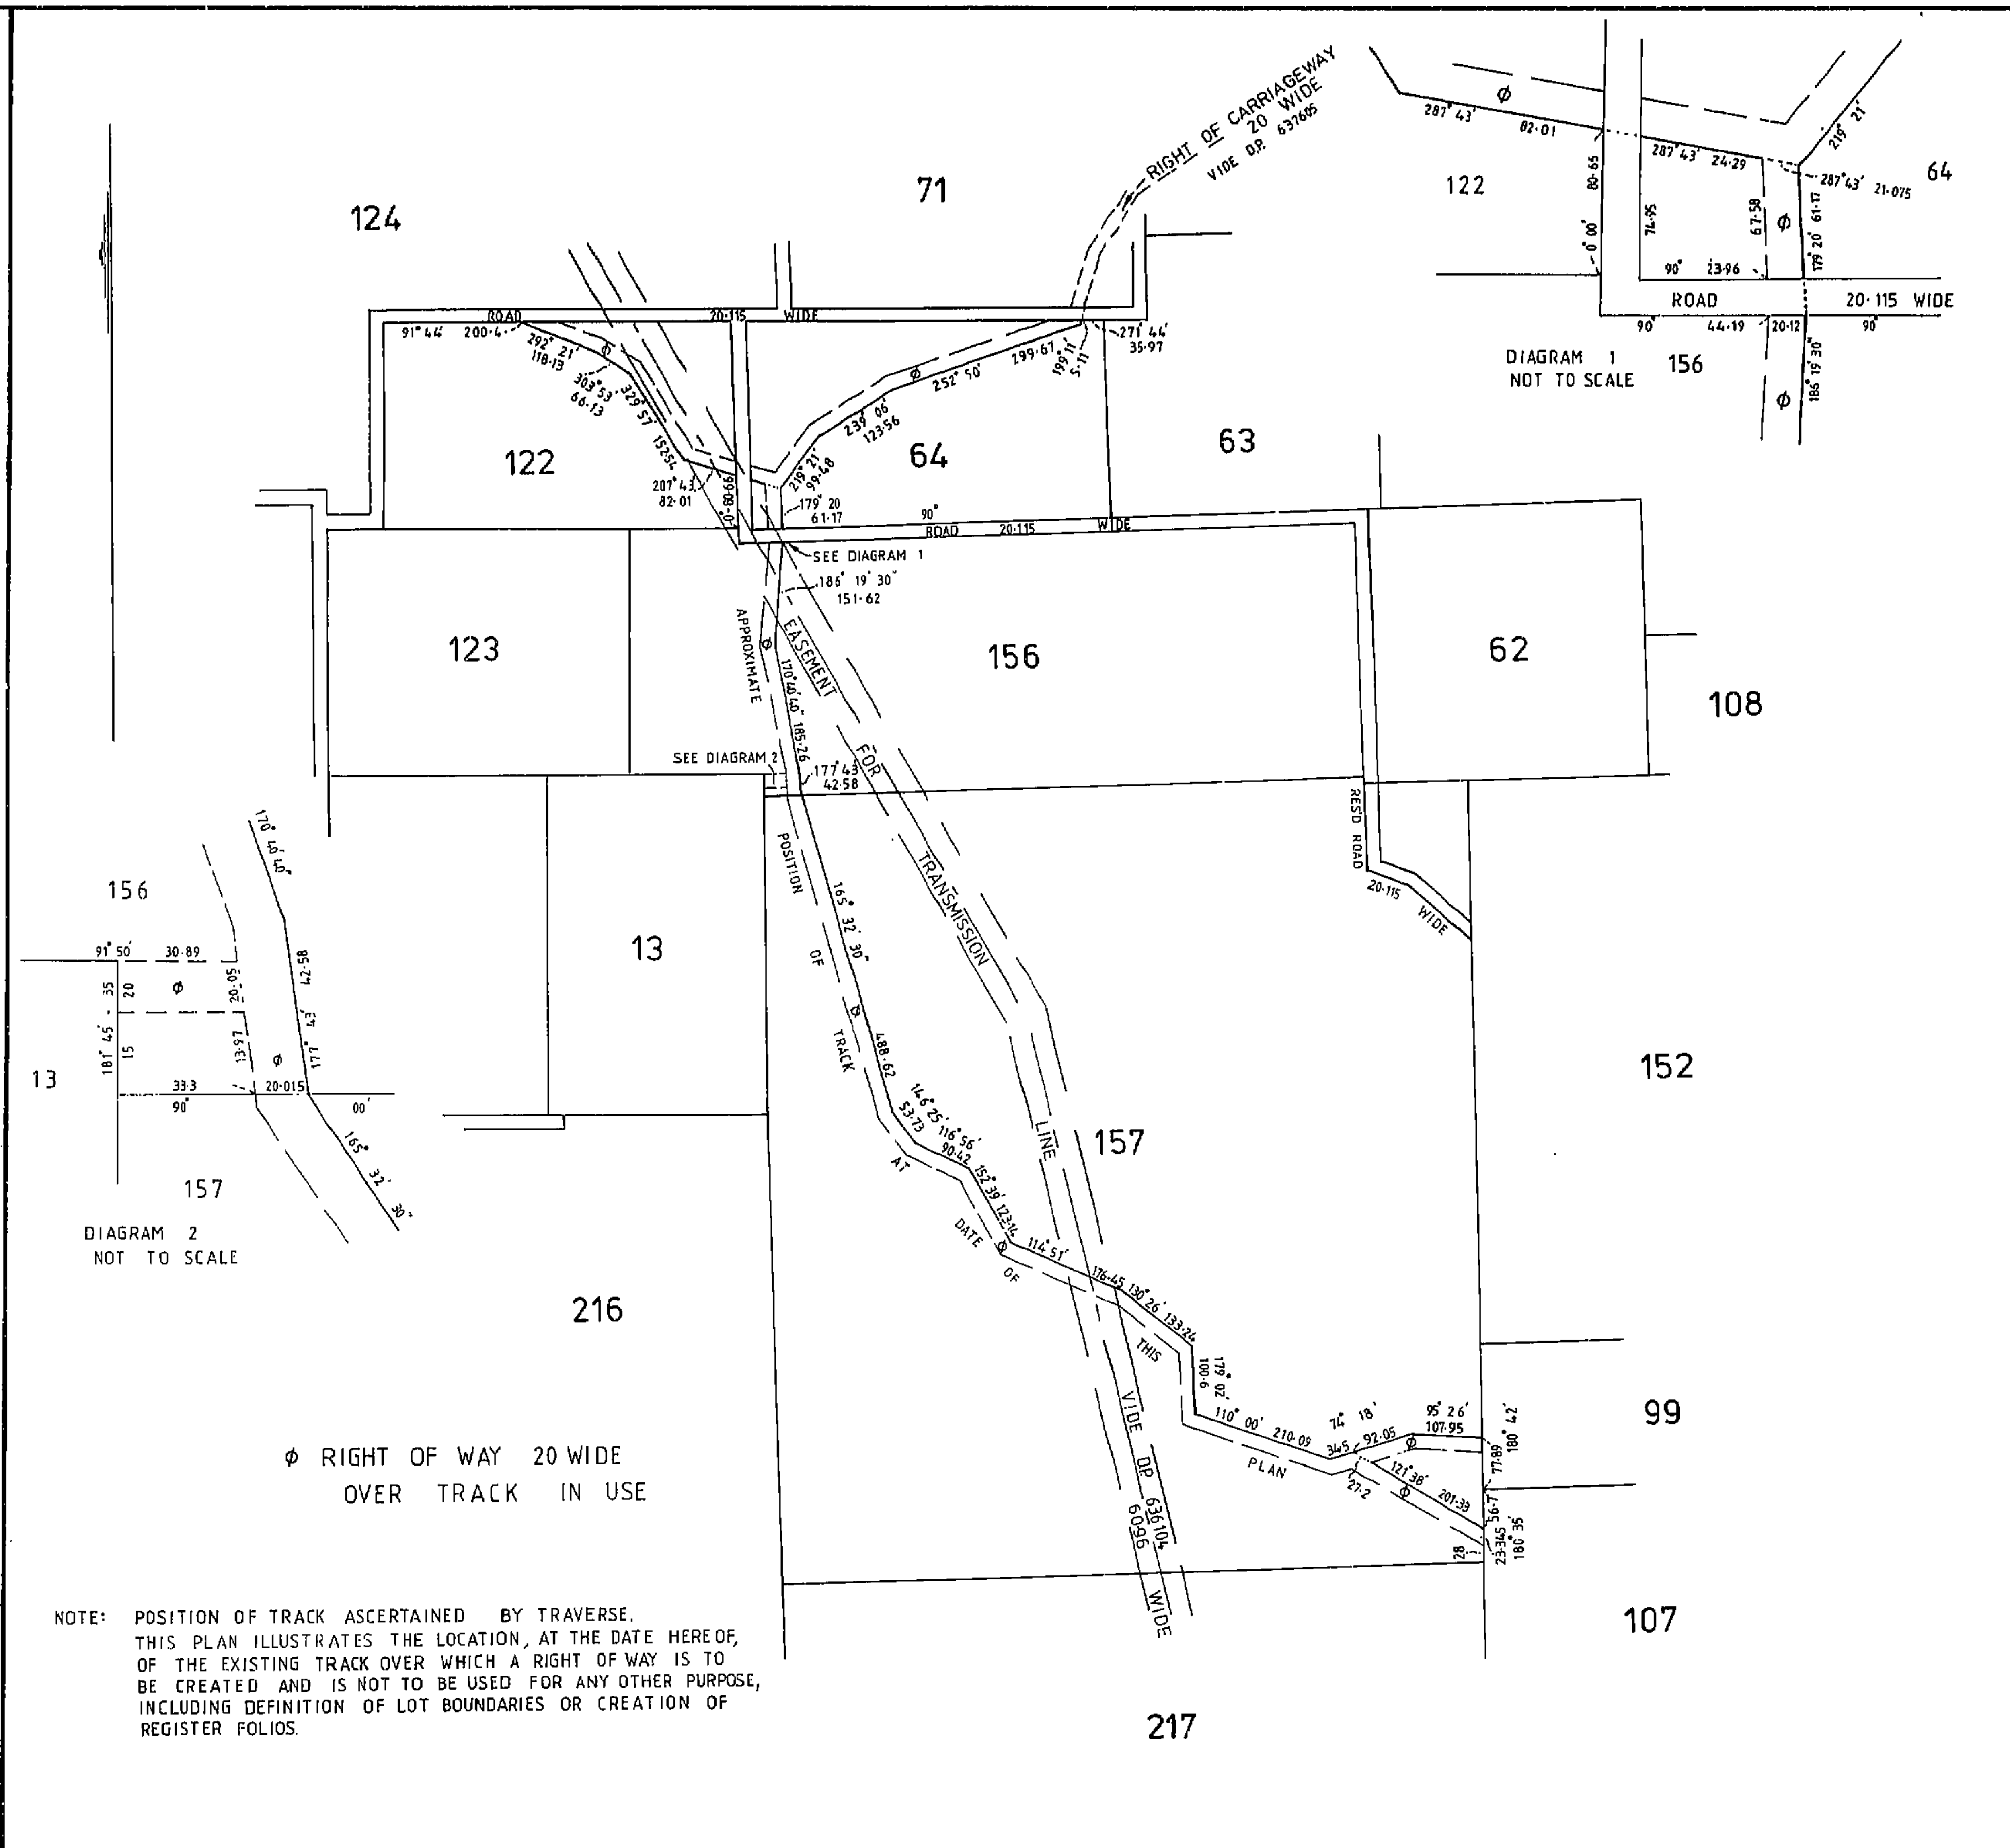

NOTE: POSITION OF TRACK ASCERTAINED BY TRAVERSE. THIS PLAN ILLUSTRATES THE LOCATION, AT THE DATE HEREOF, OF THE EXISTING TRACK OVER WHICH A RIGHT OF WAY IS TO BE CREATED AND IS NOT TO BE USED FOR ANY OTHER PURPOSE, INCLUDING DEFINITION OF LOT BOUNDARIES OR CREATION OF REGISTER FOLIOS.

Council Clerk's Certificate

I hereby certify that –

(a) the requirements of the Local Government Act, 1919 (other than the requirements for the registration of plans), and

*(b) the requirements of section 34B of the †Metropolitan Water, Sewerage and Drainage Act, 1924, as amended. †Hunter District Water, Sewerage, and Drainage Act, 1938, as amended

have been complied with by the applicant in relation to the proposed .... (Insert "new road", "subdivision" or "consolidated lot") set out herein

Subdivision No. ....

Date ....

(Signature) ....
Council Clerk

*This part of certificate to be deleted where the application is only for a consolidated lot or the opening of a new road or where the land to be subdivided is wholly outside the areas of operations of the Metropolitan Water Sewerage and Drainage Board and the Hunter District Water Board.
†Delete if inapplicable.

MPD

Table of mm

WARNING: CREASING OR FOLDING WILL LEAD TO REJECTION

D.P. 639390

Registered: 17·12·1986

C.A.: ——————

Title System: TORRENS

Purpose: EASEMENT

Ref. Map: 8627-1-S^II

Last Plan: 266-1793 461-1793 966-1793 967-1793

PLAN OF RIGHT OF WAY OVER PORTIONS 64, 122 156 & 157

Reduction Ratio 1: 7500
Lengths are in metres.

~~Mun.~~/Shire ~~City~~ YASS

Locality: 'THE HORSESHOE'

Parish: UMBURRA

County: COWLEY

~~This is sheet 1 of my plan in~~ ———— sheets.
(Delete if inapplicable).

I, JAMES WILBUR SAWKINS of 53 COLBEE COURT, PHILLIP, ACT. a surveyor registered under the Surveyors Act, 1929, as amended, hereby certify that the survey represented in this plan is completed from (C.186.C467.C.96.C967) 1793 ~~is accurate and has been made *(1) by me (2) under my immediate supervision in accordance with the Survey Practice Regulations, 1933,~~ and was completed on † 15th OCTOBER 1986

Signature James Sawkins
Surveyor registered under Surveyors Act, 1929, as amended.
Datum Line of Azimuth.
*Strike out either (1) or (2). †Insert date of survey.

Panel for use only for statements of intention to dedicate public roads or to create public reserves, drainage reserves, easements or restrictions as to user.

PURSUANT TO SEC 88 B OF THE CONVEYANCING ACT IT IS INTENDED TO CREATE -
RIGHT OF WAY 20 WIDE

SURVEYOR'S REFERENCE 85415

Y	O	O	O	F	I	B

This negative is a photograph made as a permanent record of a document in the custody of the Registrar General this day.

17th December, 1986