

PLANFORM 2

SIGNATURES, SEALS AND STATEMENTS of intention to dedicate public roads or to create reserves, drainage reserves, easements, restrictions on the use of land or positive covenants.

As mortgagee under mortgage number Y42706 Westpac Banking Corporation hereby consents to the within Plan of Subdivision.

Westpac Banking Corporation

by its Attorney

who hereby states that at the time of executing this instrument notice of revocation has been received of the Power of Attorney registered at the office of the Registrar General No. 214 Book 3223 which is the authority of which this instrument has been executed.

Commercial Manager
New South Wales Division

Signed in behalf of
Westpac Banking Corporation by
[Signature]
Its duly authorised Attorney
who is a Solicitor of the Supreme Court of New South Wales

AS MORTGAGEE UNDER MORTGAGE NUMBER Y427102, THE HORSESHOE PTY LTD hereby consents to the within Plan of Subdivision.

THE COMMON SEAL OF THE HORSESHOE PTY LTD was hereunto affixed in accordance with its Articles of Association and in the presence of

[Signature]
Director

Crown Lands Office Approval

PLAN APPROVED

Land District

Field Book

Council Clerk's Certificate


I hereby certify that:
(a) the requirements of the Local Government Act, 1919 (other than the requirements for the registration of plans), and
(b) the requirements of Part 3 Division 2 of the Water Board Act, 1902 and the Water Supply Authorities Act, 1907
have been complied with by the applicant in relation to this proposed SUBDIVISION.
Subdivision No. 1 of 1992
Date: 14th SEPTEMBER 1992
[Signature]
Council Clerk

Council File No.

2073P

*This part of certificate to be deleted where the application is only for a consolidated lot or the opening of a new road or where the land to be subdivided is wholly outside the area of operation of the Water Board Act, 1902 and the Water Supply Authorities Act, 1907.
† Delete if inapplicable

SURVEYOR'S REFERENCE: A/57 KM

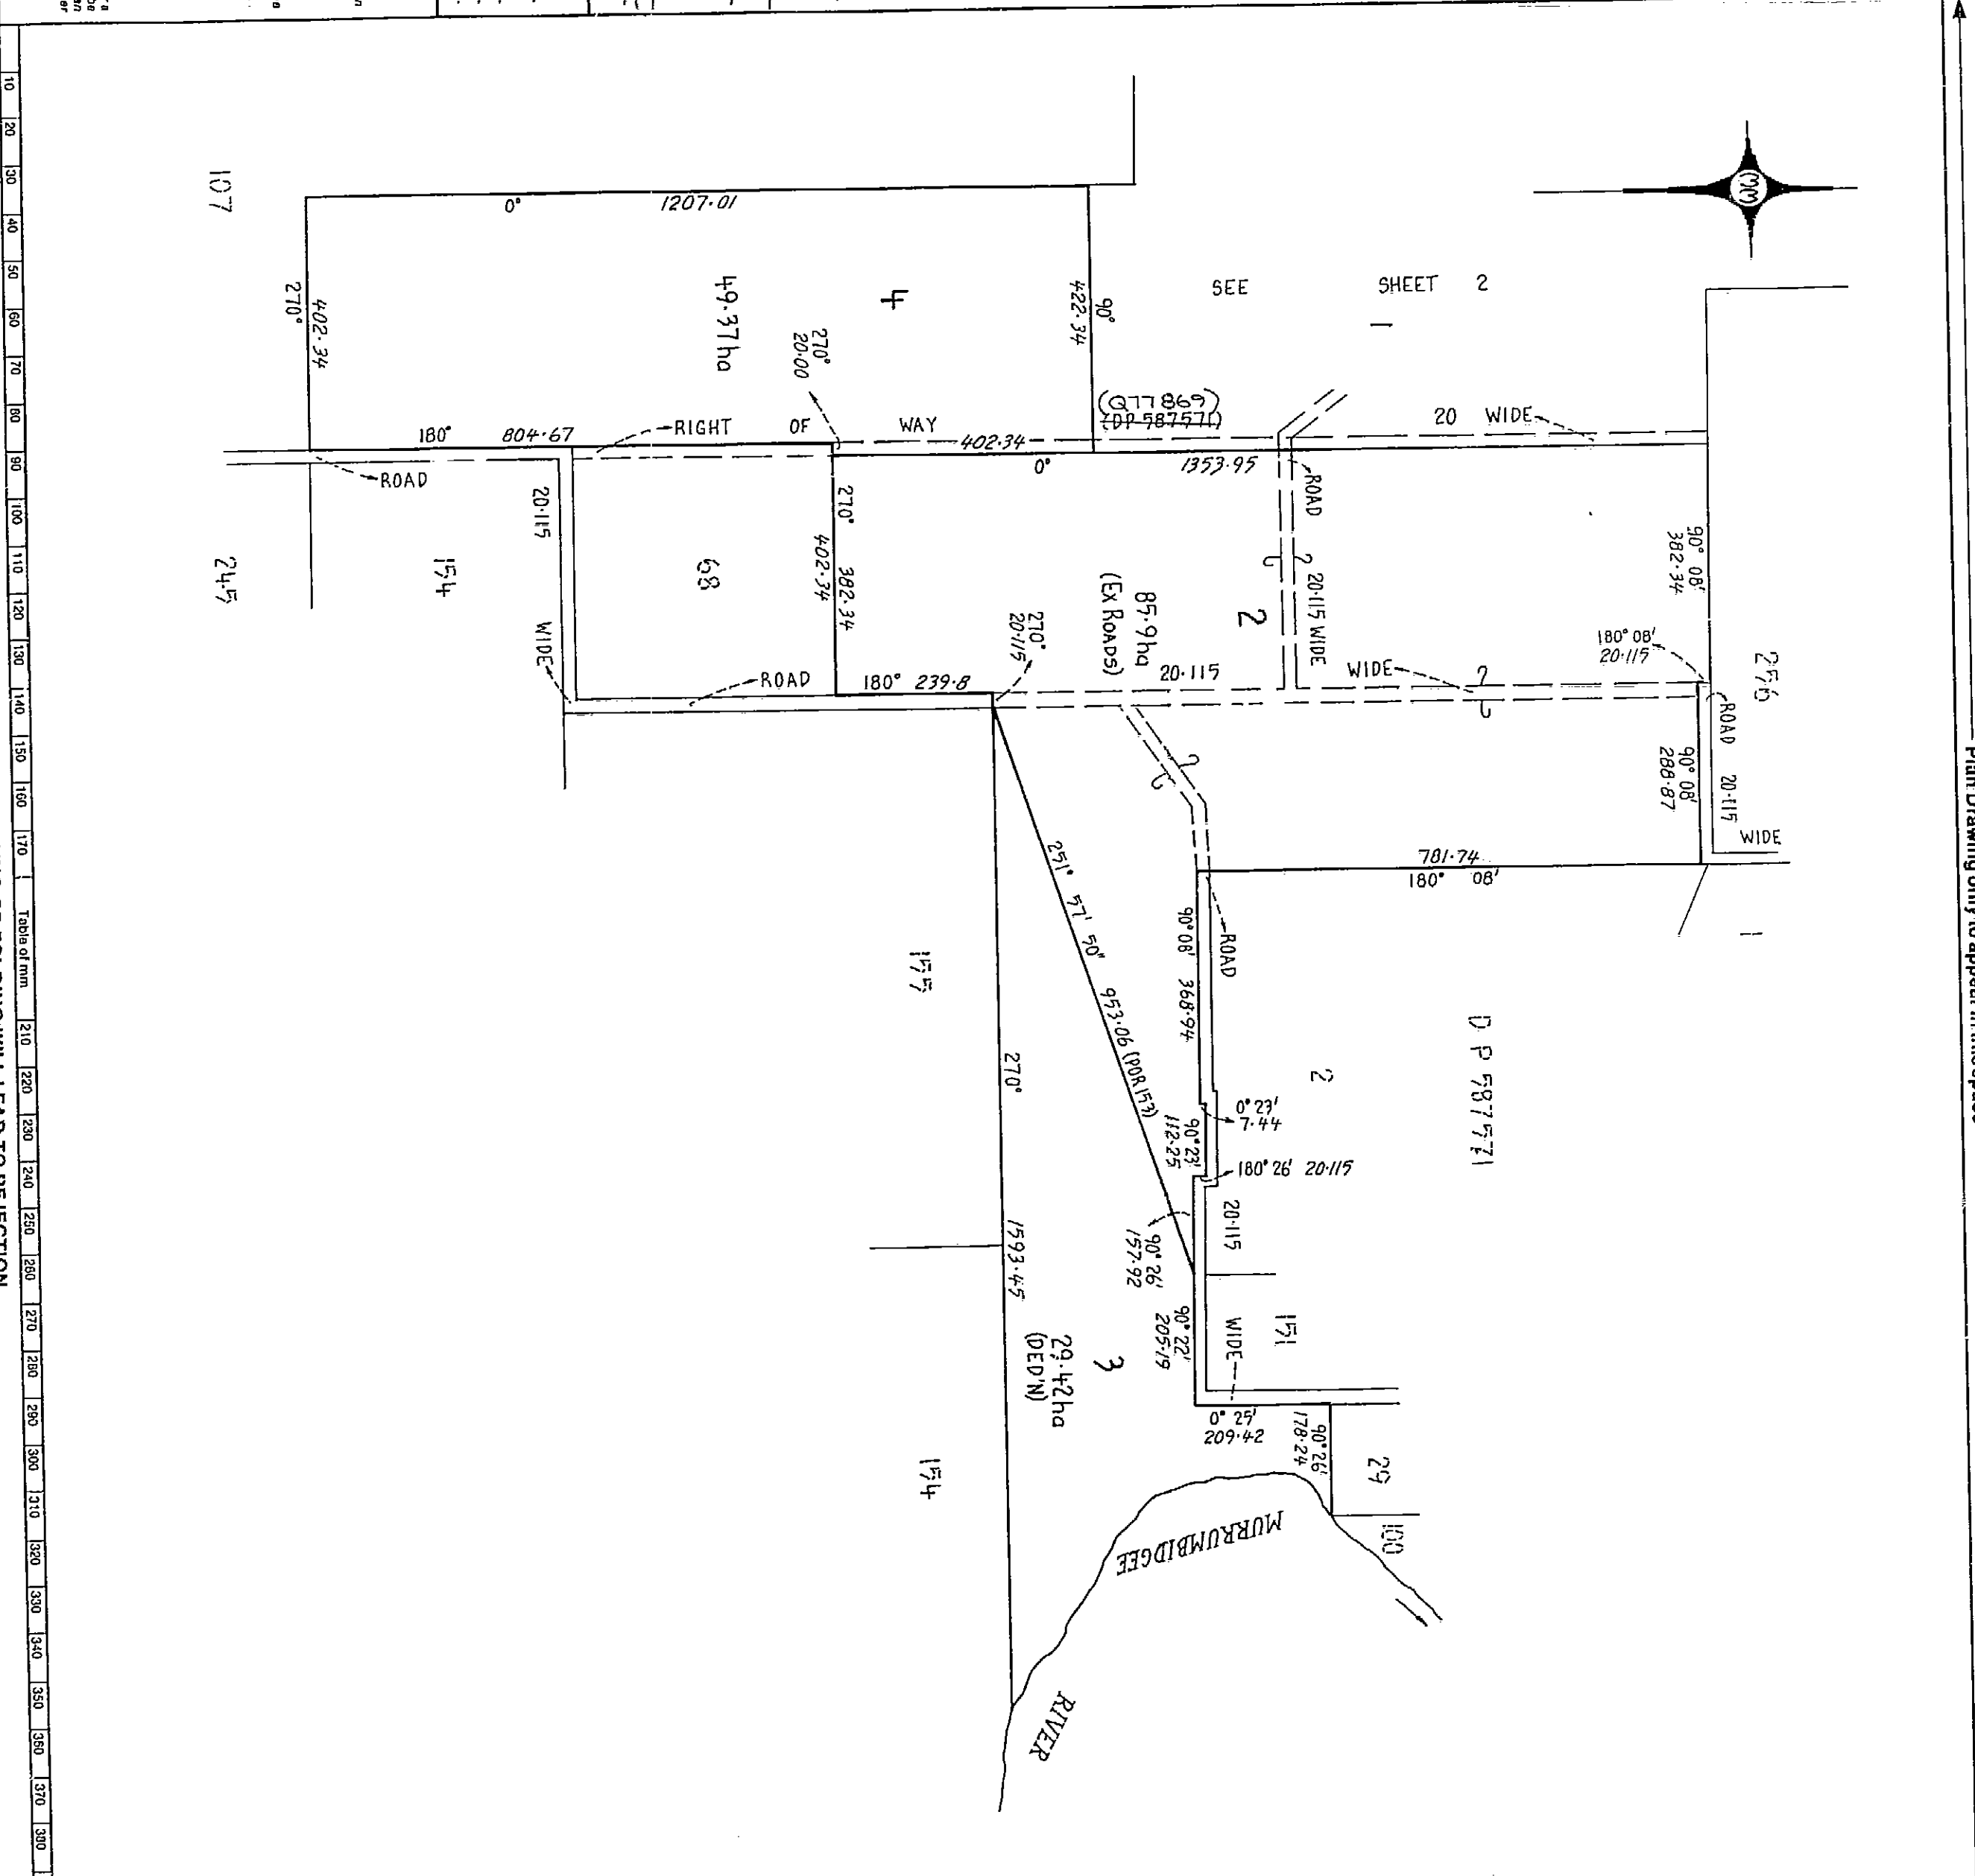

Plan Drawing only to appear in this space

OFFICE USE ONLY

DP 806324

Registered: 23.11.1990

CA: N° 18/1990 OF 14-9-90

Title System: TORRENS

Purpose: SUBDIVISION

Ref. Map: 8627-1-S

Last Plan:

PLAN OF SUBDIVISION OF
PORTIONS 69, 99, 152 & 173

Lengths are in metres. Reduction Ratio: 1:500

Murrumbidgee

Locality: THE HORSESHOE

Parish: UMBURRA

County: COWLEY

This is sheet 1 of my plan in 2 sheets.
(Delete if inapplicable)

ALLAN JEFFREY MAIL

of PO BOX 54, JANISON, CENTRE ACT, 2614.

a surveyor registered under the Surveyors Act, 1924, as amended, hereby certifies that the survey represented in this plan is a true and correct survey.

Plans used in preparation of survey/compilation:
C962 - 1793
C963 - 1793
C268 - 1793
DP 987571
C930 - 1793

PANEL FOR USE ONLY for statements of intention to dedicate public roads or to create public reserves, drainage reserves, easements or restrictions as to user.

PURSUANT TO SEC 88B OF THE CONVEYANCING ACT 1919 AS AMENDED IT IS INTENDED TO CREATE -

1. RESTRICTION AS TO USER

2. RESTRICTION AS TO USER

WARNING: CREASING OR FOLDING WILL LEAD TO REJECTION

This negative is a photograph made as a permanent record of a document in the custody of the Registrar General this day. 26th November, 1990



10 20 30 40 50 60 70 Table of mm 110 120 130 140

PLAN FORM 3

To be used in conjunction with Plan Form 2

WARNING: CREASING OR FOLDING WILL LEAD TO REJECTION

OFFICE USE ONLY

DP 806324

Registered: 23.11.1990

This is sheet 2 of my plan in 2 sheets
dated 4.9.90

Surveyor registered under Surveyors Act 1928



This is sheet 2 of the plan of 2
sheets covered by my Certificate No.
1511990 of 14/9/90

For use where space is insufficient in any panel on Plan
Form 2.

[Signature]
Council Clerk

Reduction Ratio 1: 7500

Plan Drawing only to appear in this space

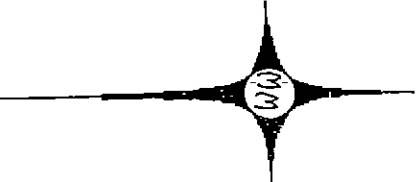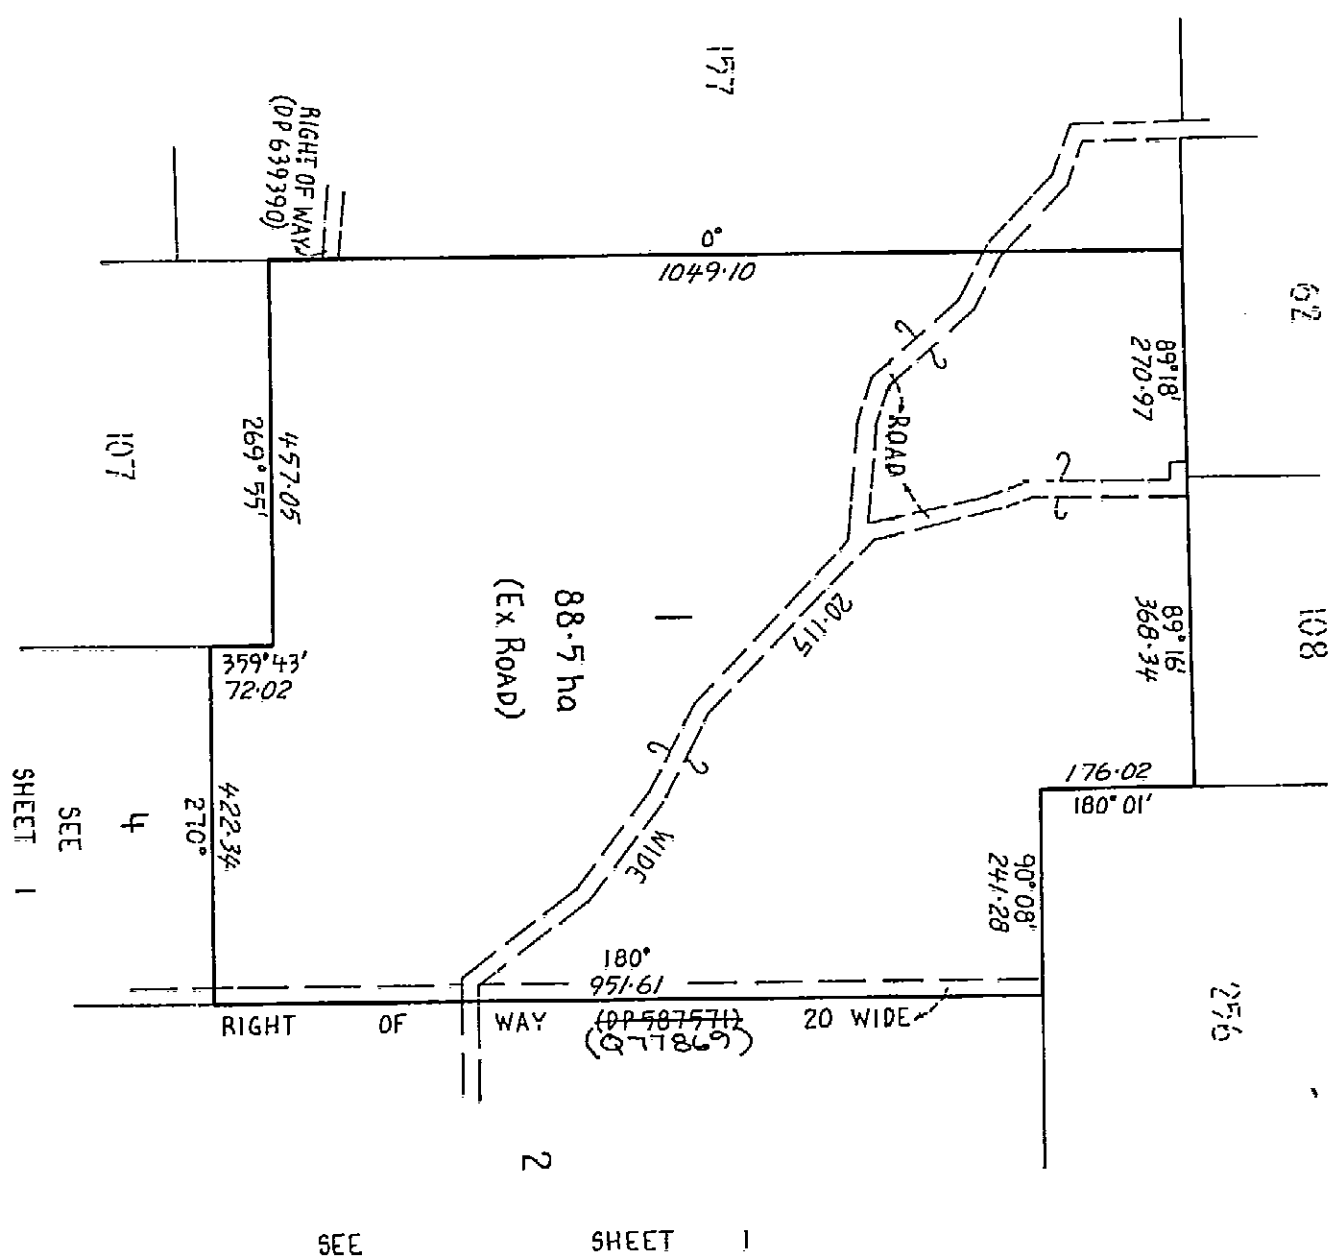

2

10	20	30	40	50	60	70	Table of mm	110	120	130	140
----	----	----	----	----	----	----	-------------	-----	-----	-----	-----

This negative is a photograph made as a permanent
record of a document in the custody of the
Registrar General this day. 26th November, 1990

