


PLAN FORM 3

To be used in conjunction with Plan Form 2

WARNING: CREASING OR FOLDING WILL LEAD TO REJECTION

OFFICE USE ONLY

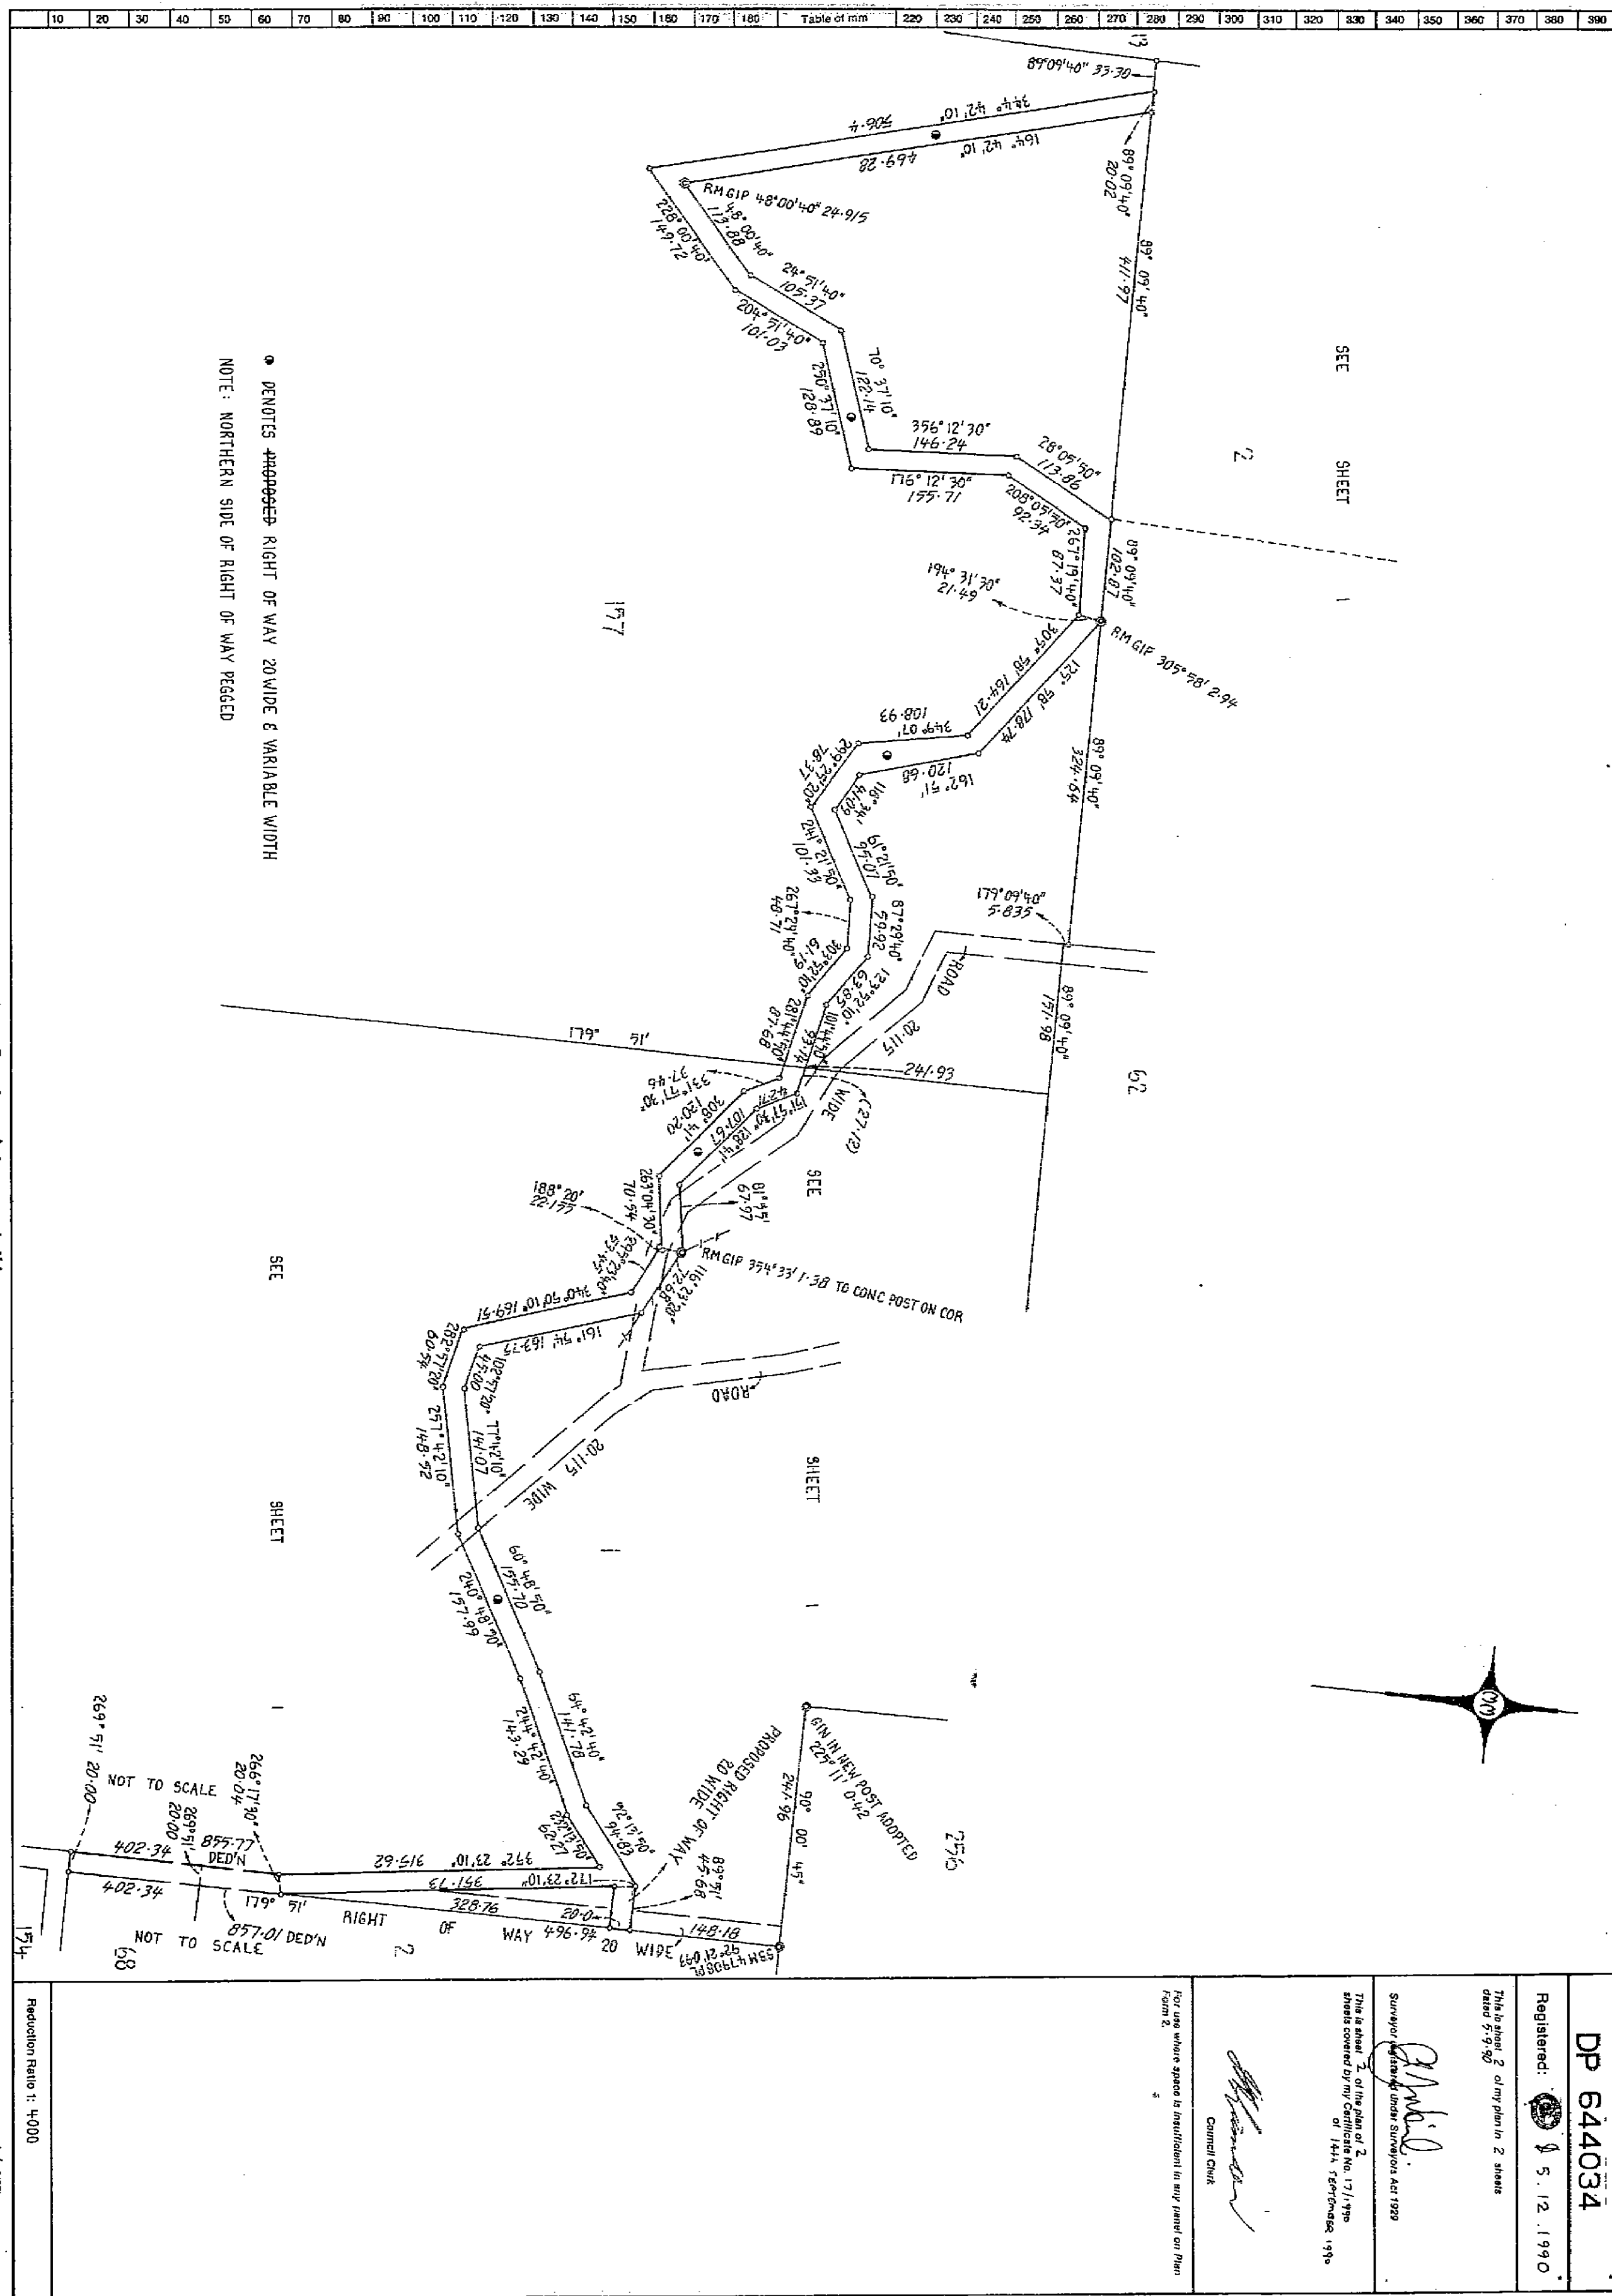

• DENOTES PROPOSED RIGHT OF WAY 20 WIDE & VARIABLE WIDTH
NOTE: NORTHERN SIDE OF RIGHT OF WAY PEGGED

Plan Drawing only to appear in this space

Reduction Ratio 1: 4000

10	20	30	40	50	60	70	Table of mm	110	120	130	140
This negative is a photograph made as a permanent record of a document in the custody of the Registrar General this day, 6th December, 1990											

